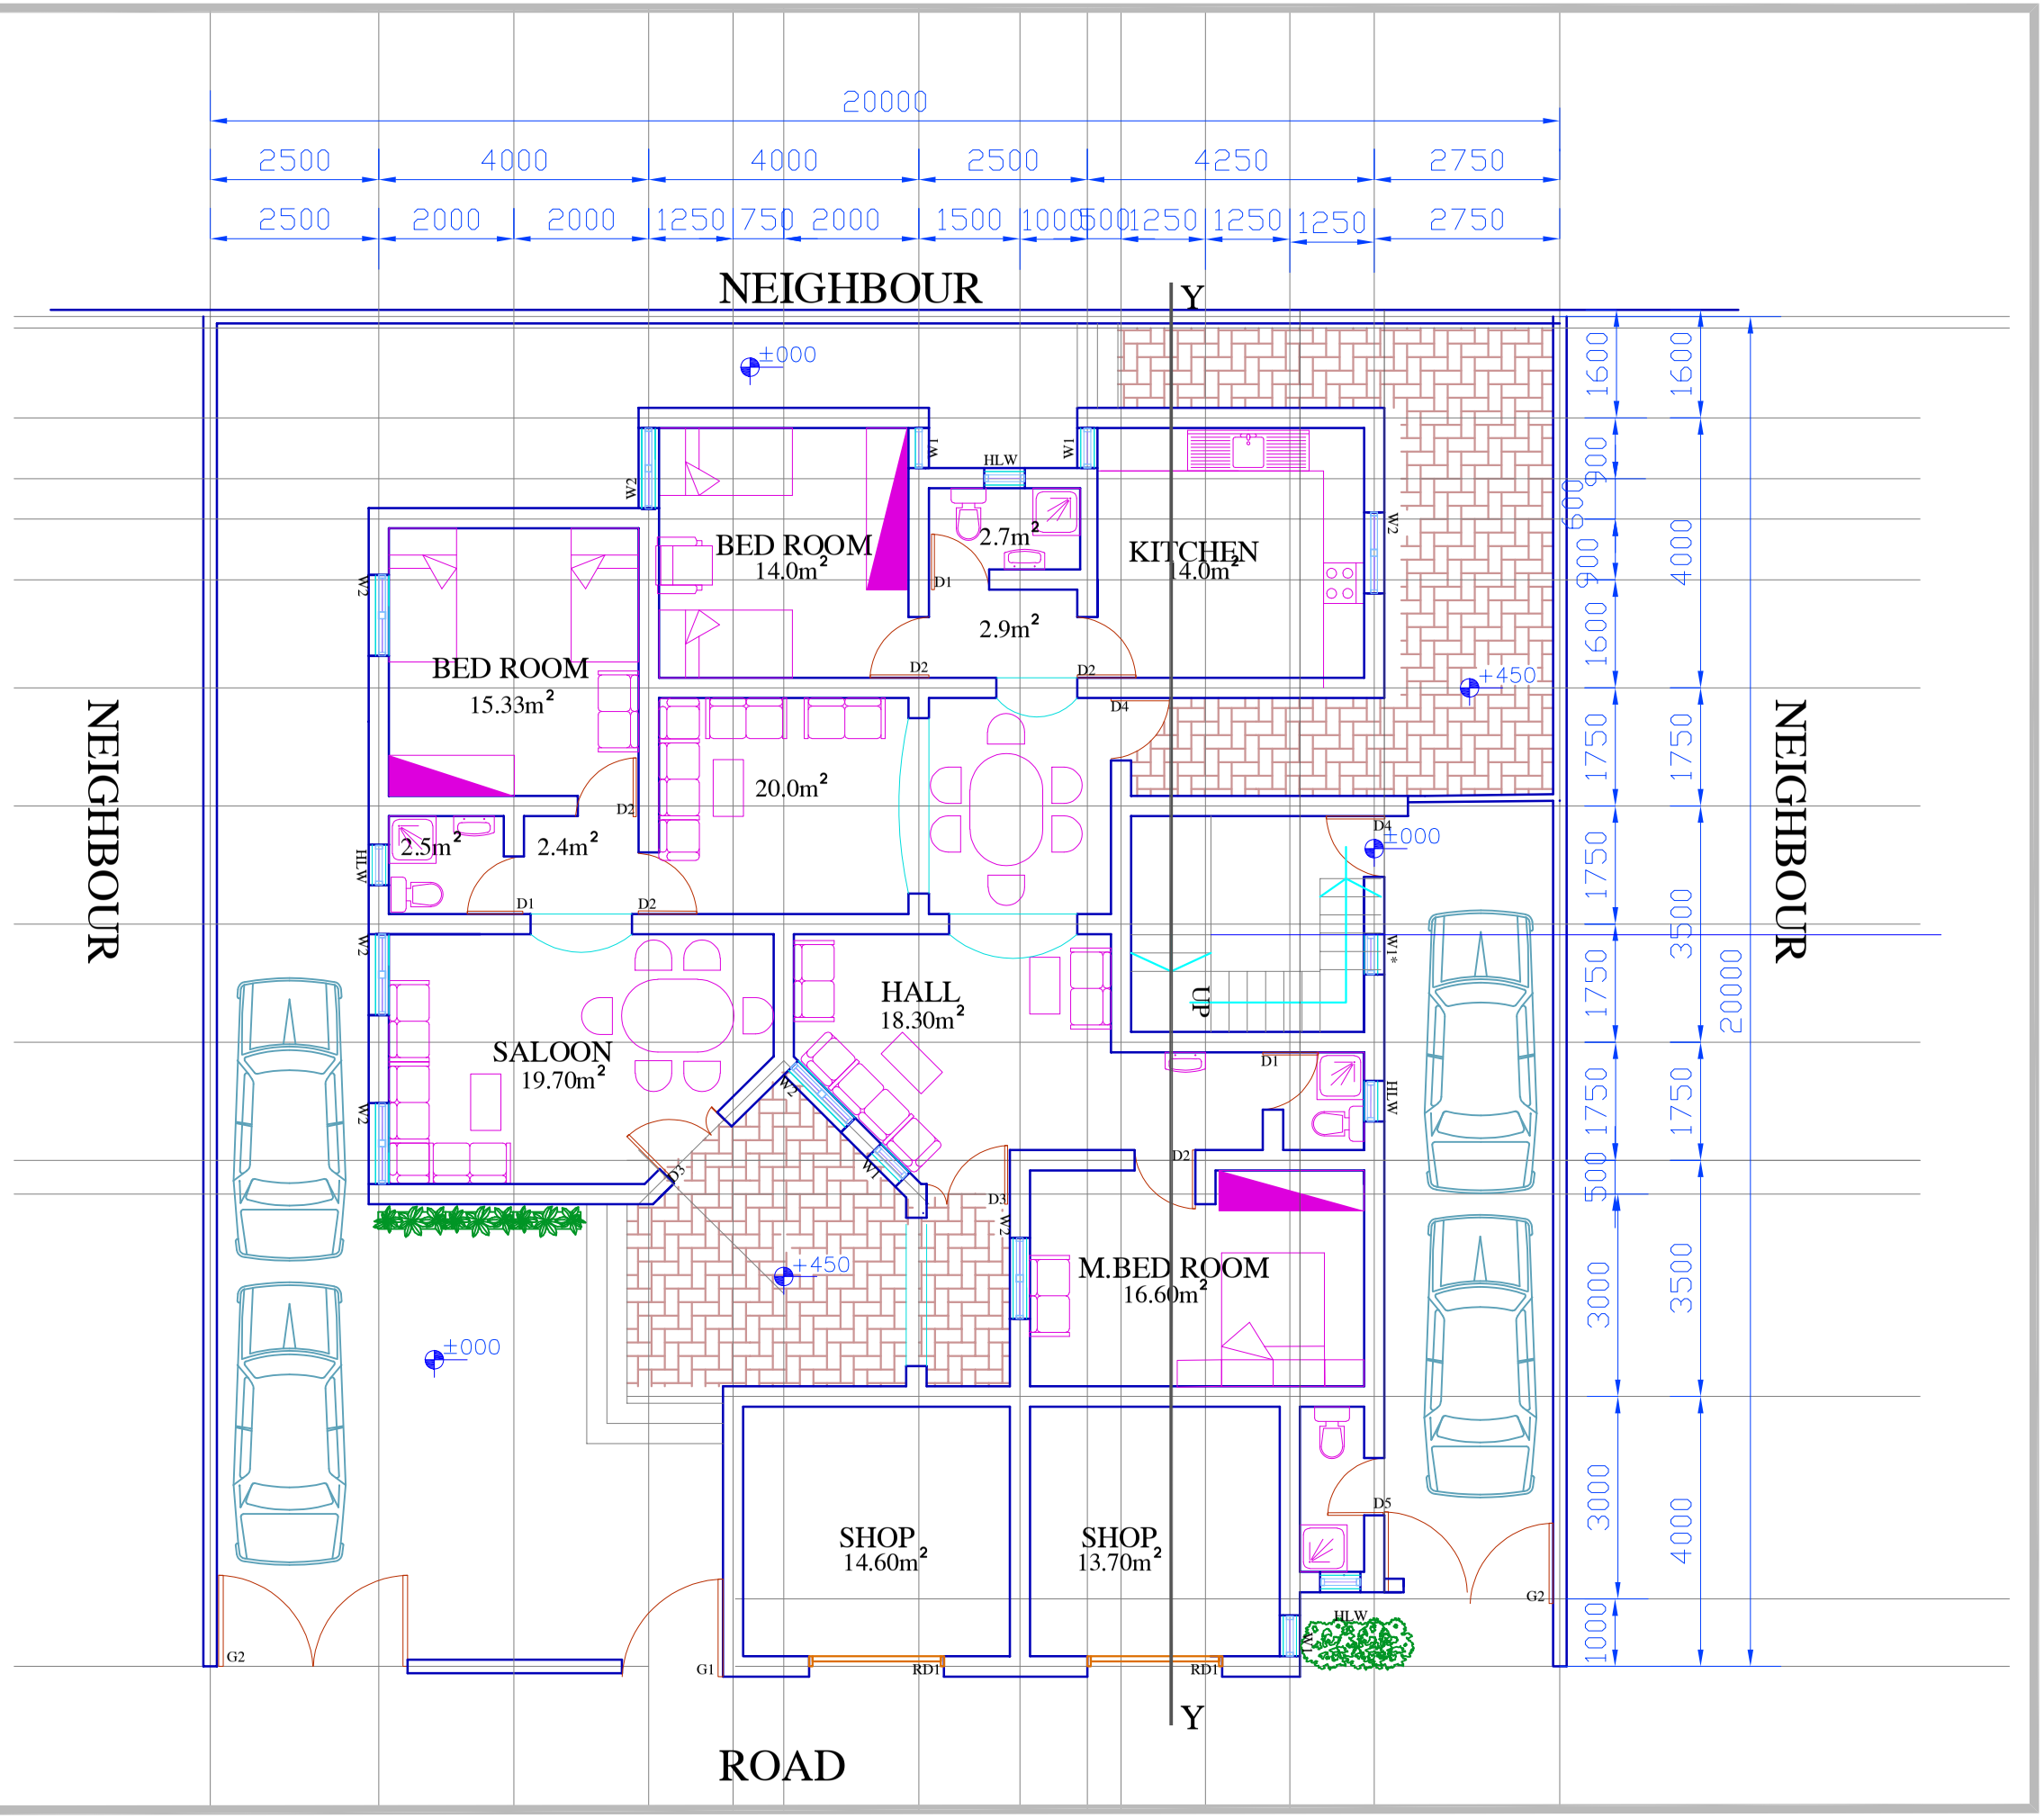


PROJECT:RESIDENTIAL HOUSE

DOORS & WINDOWS SCHEDULE

OPENING	DIMENSION (width x hight)	MATERIAL	No
W .1.	600 x1200	ALUMINUIM	5
W .2.	1200 x 1200	ALUMINUIM	7
H . L . W.	600 x 600	ALUMINUIM	4
D .1.	750 x 2150	ALUMINUIM	3
D .2.	900 x 2150	ALUMINUIM	5
D .3.	1200x 2150	WOOD	2
D .4.	1000x 2150	WOOD	2
D .5.	750 x 2150	STEEL	1
G.1.	1500x2150	STEEL	1
G.2.	2700x2150	STEEL	2
R.D.	2500x2500	STEEL	2

W : Window D : DOOR G : GATE
H.L.W :HIGH LEVEL WINDOW
RD : ROLLUP SHUTTER DOOR

Approved For

Client:

Authority:

Construction:

CLIENT :

LOCATION :PLOT NO: BLOCK: -

DESIGNED BY : NESRIEN MOHAMMED OSMAN

DRAWN BY : N-M-O

DATE :JUNE 2026 | **Sh.A1** | **Rev 00**

DESIGN DRAWINGS- ARCHITECTURAL

GROUND FLOOR PLAN - SCALE 1:100